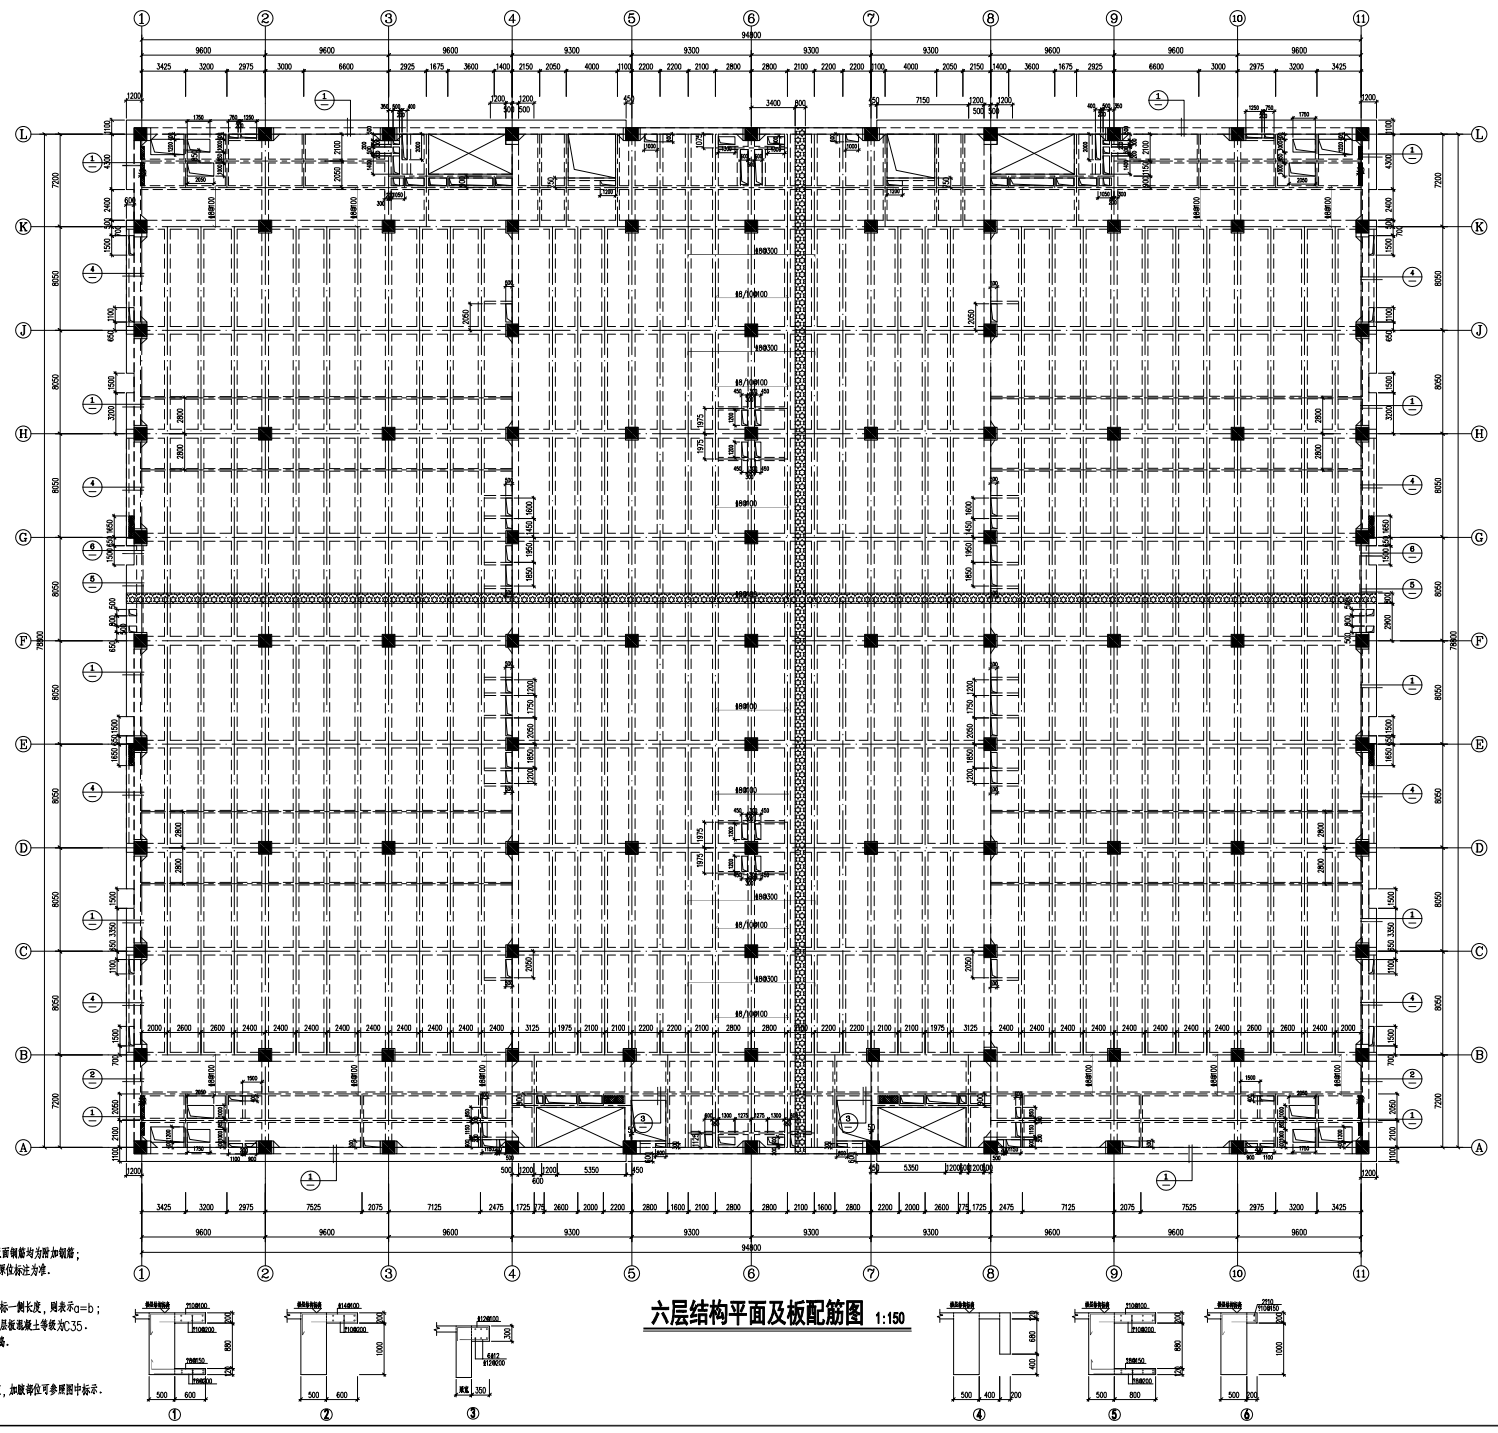

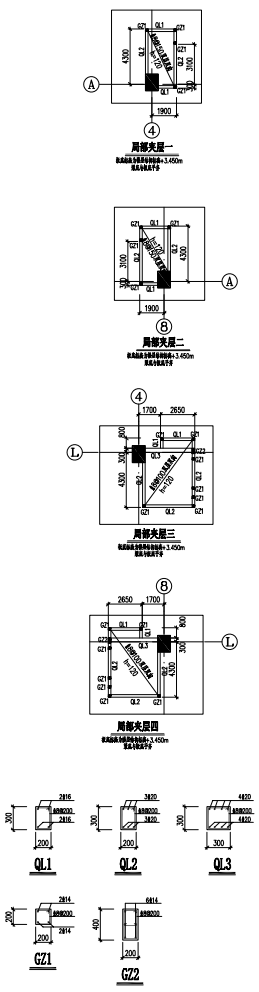

六层结构平面及板配筋图 1:150

板设计说明：

1. 本层楼板，板面设置ø10@150双向钢筋，图中绘出的板面钢筋均为附加钢筋；
   板底设置ø10@200双向钢筋，图中绘出板底筋的，以原位标注为准。
2. 图中板面钢筋均按照充分利用钢筋强度锚入梁或墙内。
   楼板支座处负筋图示「a ⊔ b」表示为 a ⊔ b；若只标一侧长度，则表示a=b；
3. 图中未注明板厚均为120mm，板面标高详图示平面；本层板混凝土等级为C35。
4. ▒▒▒ 为设备管井，预留钢筋待设备安装完毕后二次浇捣。
5. 填充墙下无梁处，在板内布2Φ16板底加强钢筋。
6. 洞口较大详结构设计总说明。
7. 梁柱偏心较大的位置，须按照总说明要求进行梁水平加腋，加腋部位可参照图中标示。
8. ▒▒▒ 为温度后浇带。

楼层	层高(m)	底标高(m)	混凝土强度等级	抗震等级等级	混凝土强度
			C35		
无层	36.450		C35	C35	
6	30.850	5.600	C35	C35	
5	24.850	5.800	C35	C40	
4	19.050	5.800	C35	C45	
3	13.250	5.800	C35	C50	
2	7.450	5.800	C35	C60	
1	-0.050	7.500	C35	C60	
基础底下面	-5.050	5.000	C35	C60	C35
层号	标高(m)	层高(m)	混凝土强度等级	抗震等级等级	混凝土强度

中南建筑设计研究院有限公司
CENTRAL SOUTH ARCHITECTURAL DESIGN INSTITUTE CO., LTD.
设计证书甲级编号：A132001202
中国·南京 梅溪江东街 68 号

会签栏		
专业	签名	日期
结构		
电气		
暖通		
给排水		
总图		
建筑		
结构		
电气		
暖通		
给排水		
总图		

会签栏			
校对	刘伟	电气	郭中磊
结构		暖通	全辉
自控水		给排	王涛

建设单位	中冶金属国际贸易有限公司
设计阶段	施工图
设计号	2007T0004000020
分项号	2006001
项目名称	中冶金属国际贸易中心扩建项目
图纸内容	7#楼层（中央机房2）六层结构平面及板配筋图
图号	S-7-013-3
图纸版本	3
设计阶段	施工图