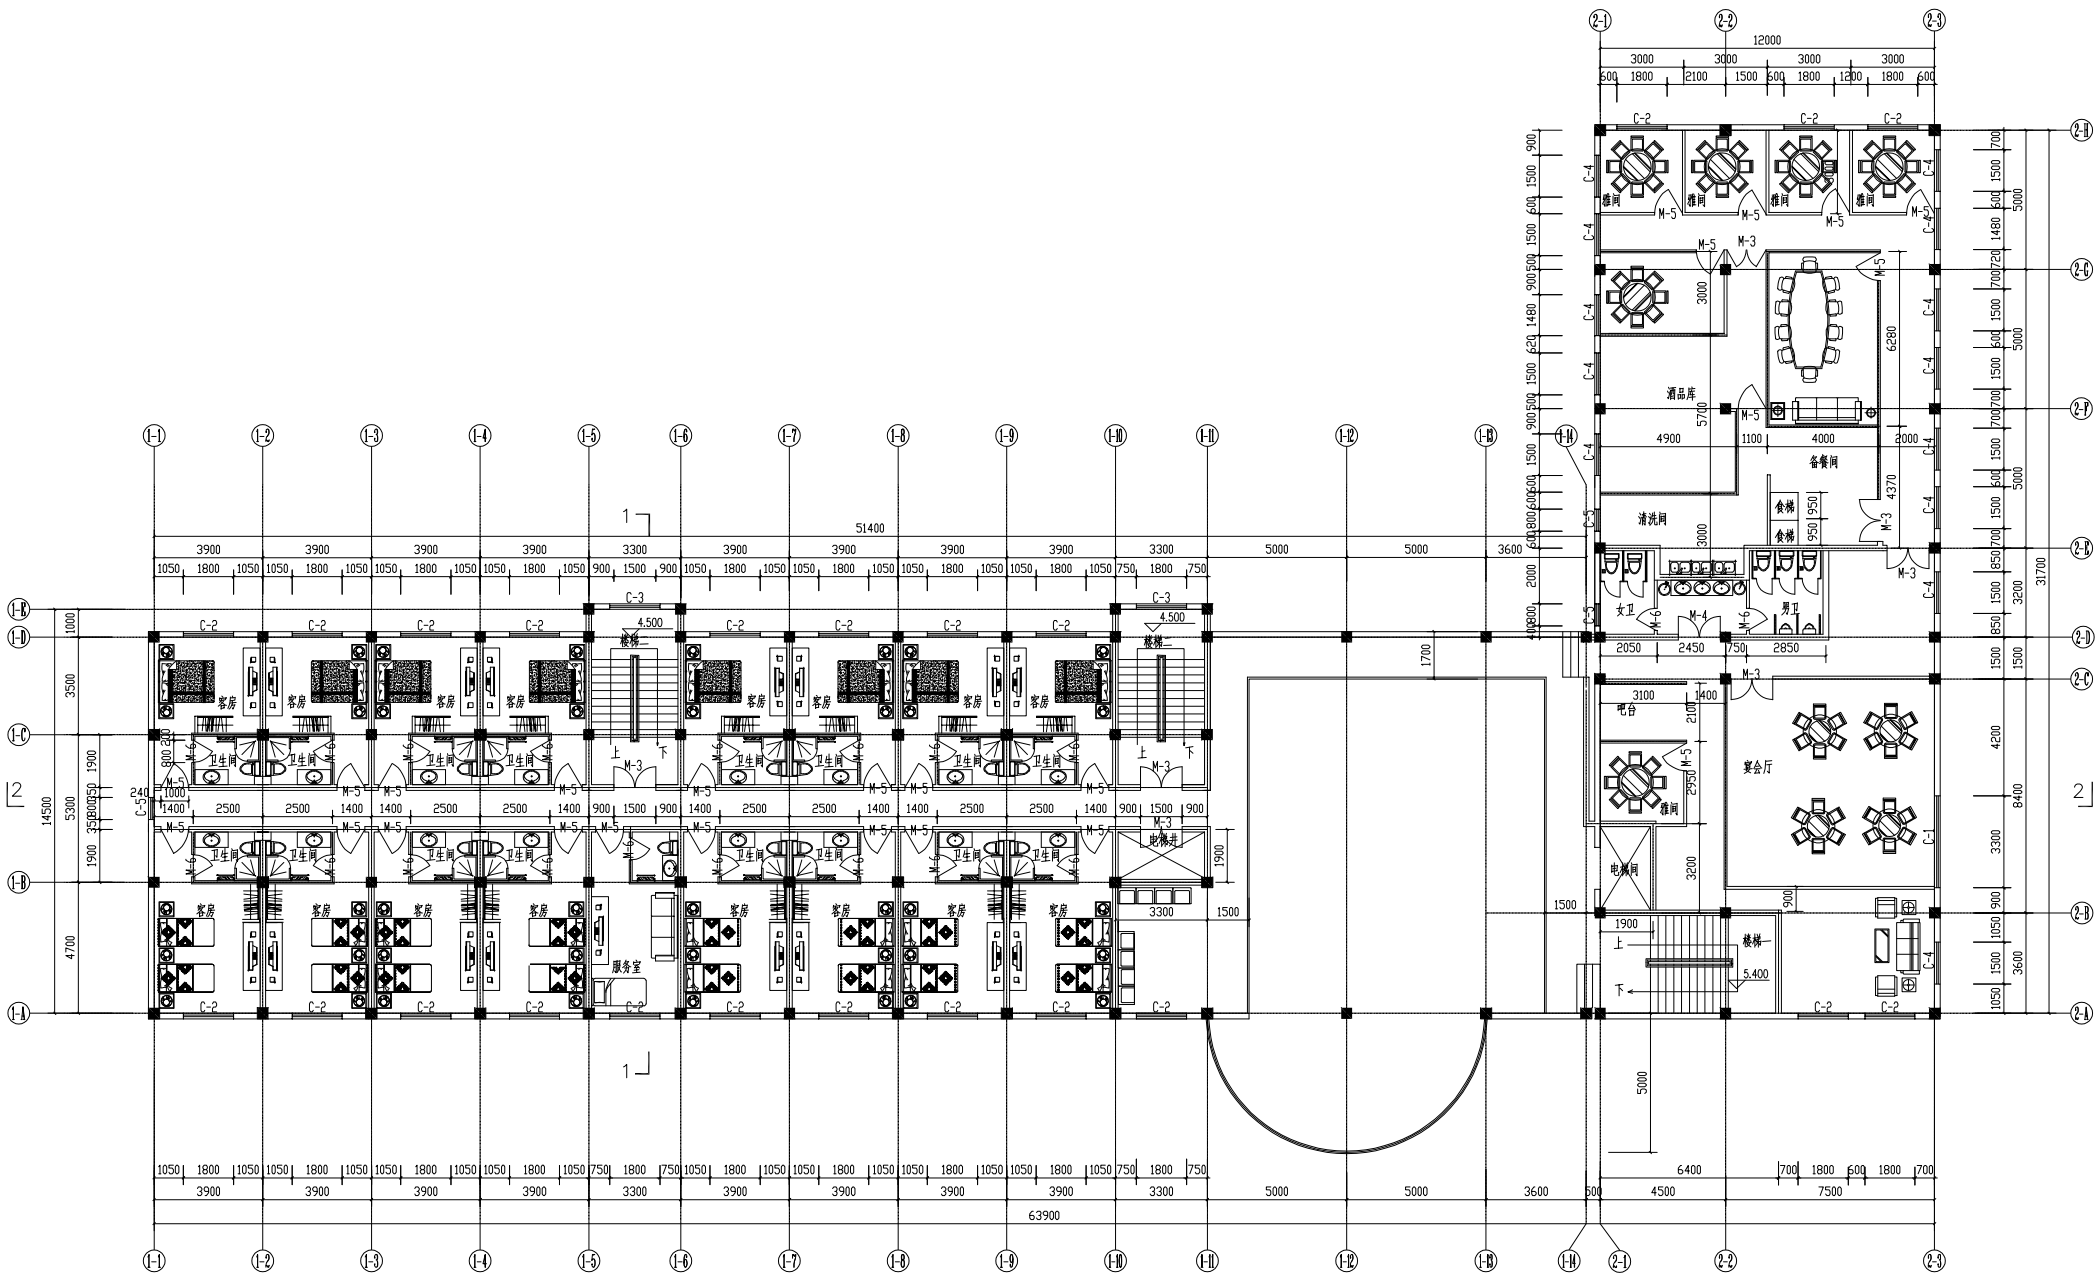

二层平面图 1:100

河北科技师范学院 土木建筑系土木工程专业			工程号		
			图号	建4-3	
审核			工程名称	金远宾馆	阶段 方案
校核		审定			专业 建筑
设计		项目负责人	图名	二层平面图	比例 1:100
制图		专业负责人			日期 2008年6月