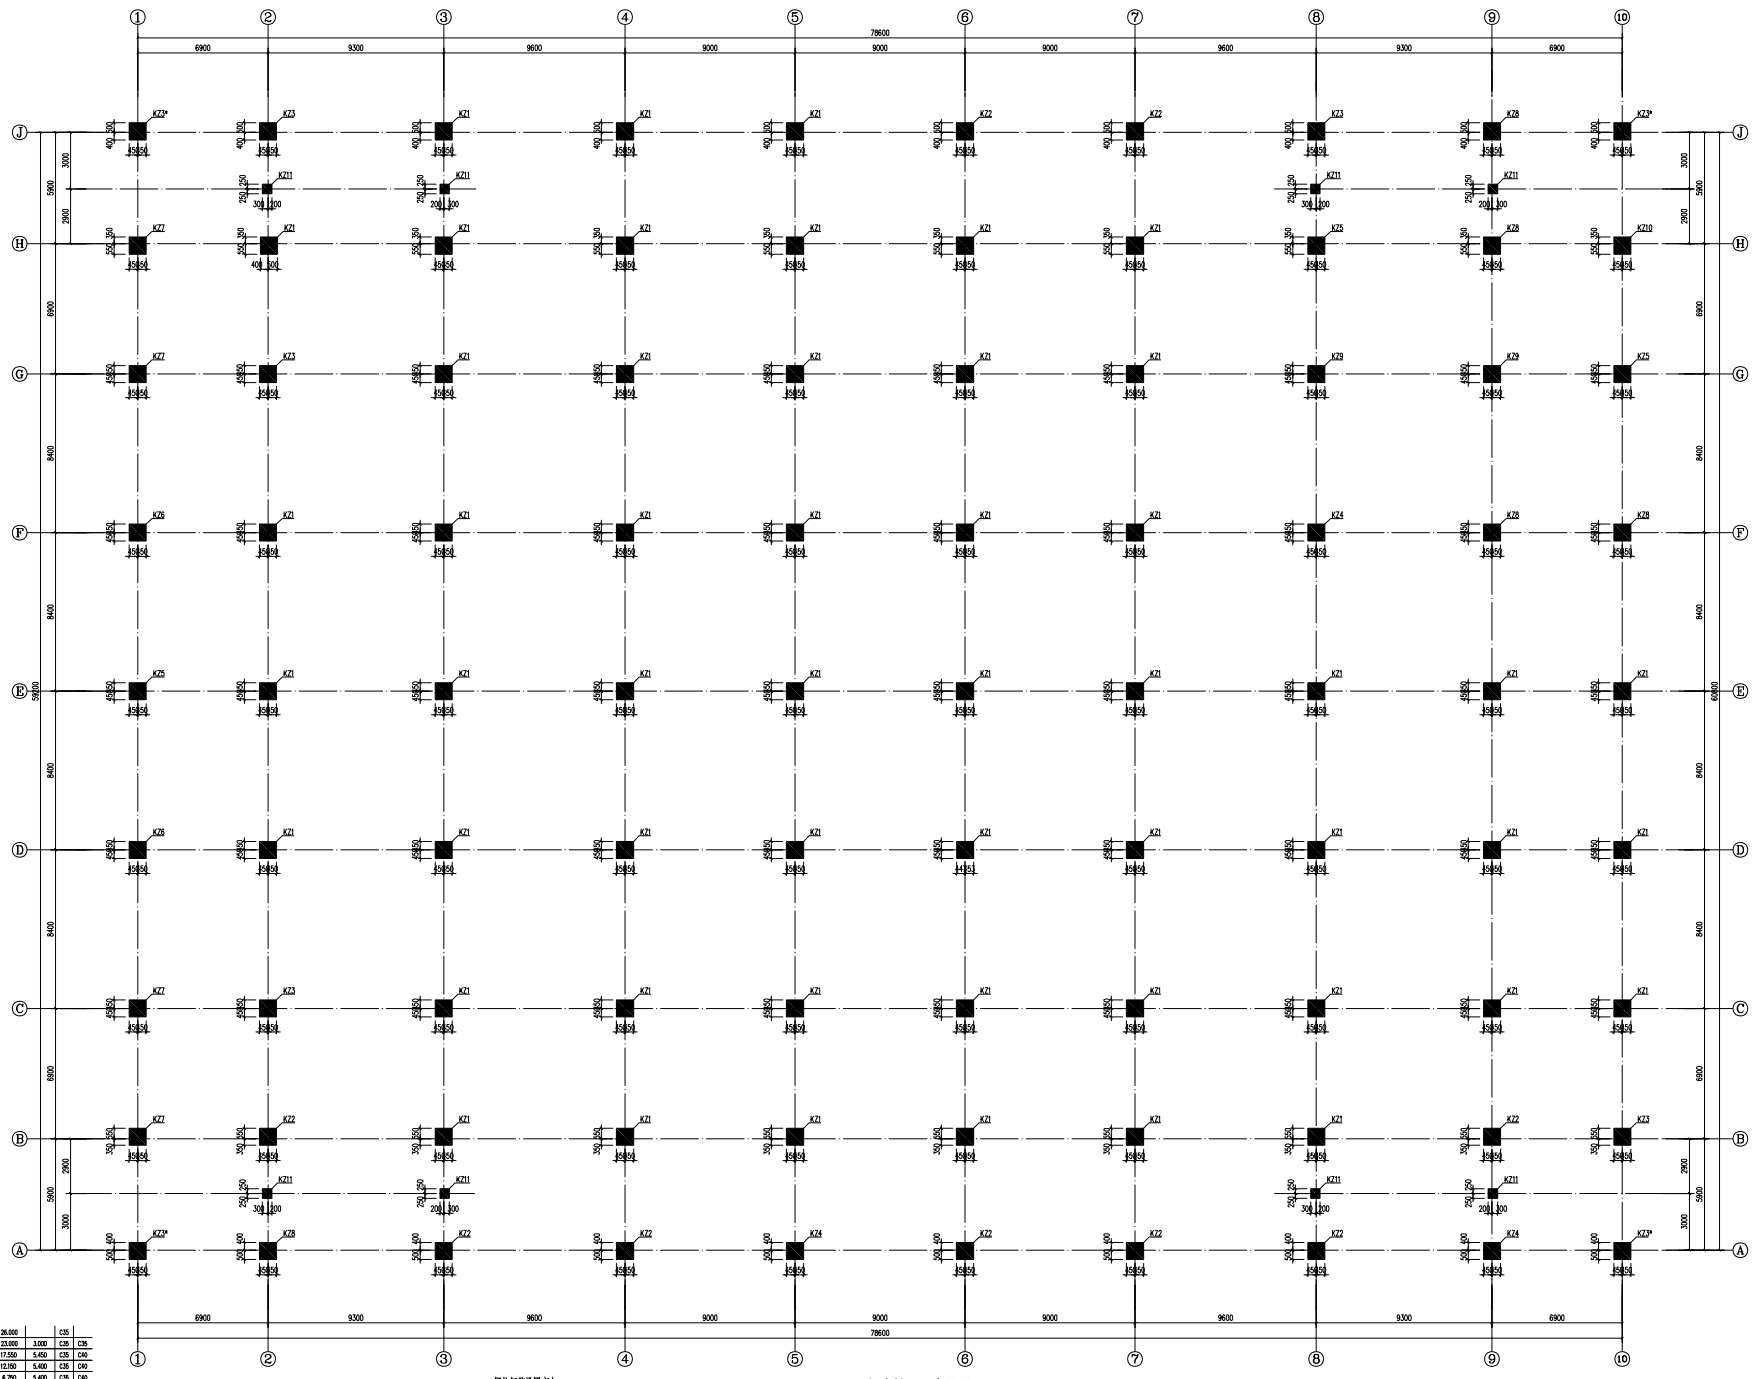

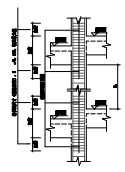

箍筋处拉筋箍筋加密区示意

柱说明：

1.本注明的柱定位均为轴线中，柱配筋详见柱配筋表.
2.柱混凝土等级为C40；钢筋:HRB400(?),HPB300(?)
除注明外，抗震柱抗震等级：二级.
3.框架柱纵筋接长应按采用电渣压力焊或机械连接头.
4.框架柱箍筋加密范围详见图集22G101-1第2-9~2-13页；
框架柱纵筋接头应采用电渣压力焊或机械连接头.
5.框架柱位于主核心区应配置箍筋，箍筋宽度、直径、间距应取节点核心区上、下柱端的箍筋较大配筋值.
6.框架柱在梁顶面处受气候影响部位加密区设置.
7.在顶板高程板顶，柱支撑顶处标高取与其相连梁板顶部标高相同.
8.配筋说明：
例：4Φ22 + 8Φ22+6Φ20
角筋 其它边筋
4Φ22 + 12Φ20
角筋 边筋
16Φ22
全部纵向钢筋

楼层	标高(m)	层高(m)	混凝土强度等级	
小屋面层	26.000		C35	
屋面层	23.000	3.000	C35	C35
4	17.550	5.450	C35	C40
3	12.150	5.400	C35	C40
2	6.750	5.400	C35	C40
1	-0.100	6.850	C35	C40
-1	基础梁		C35	C40
层号	标高(m)	层高(m)	剪力墙	柱、梁、板

楼结构层高、砼强度等级

上部结构嵌固部位：基础梁

框柱钢筋设置方向：

-0.100~6.750标高柱平面布置图 1:100

注：1. 各层框架柱混凝土强度详见层高表.
2. 带"*"的柱箍筋全高加密.
3. 柱编号仅用于本层.

序号 NO.	修改说明 REVISION DESCRIPTION	日期 DATE

本图工程未经甲方书面允许不得使用.

中华人民共和国建设部 SEAL

甲级设计单位印章名称 SEAL

CITC
CHINA INFORMATION TECHNOLOGY DESIGN AND CONSULTING INSTITUTE CO.,LTD
中讯邮电咨询设计院有限公司
国家甲级资质 · 商务部甲级 · 建设部甲级 · 甲级证书：A111005151
合格证书号 CITC-CERTIFICATE NO.

院长 PRESIDENT	
总工程师 DEPT. DIRECTOR	李 勉
审定人 AUTHORIZED FOR ISSUE BY	
项目负责人 PROJECT DIRECTOR	张庆 刘小明
审核人 AUDITED BY	杨文宜
校对人 CHECKED BY	高 银
专业负责人 DISCIPLINE RESPONSIBLE BY	白晓晨
设计人 DESIGNED BY	白晓晨

建设单位 CLIENT 北京示范区置业（河北）有限公司

工程名称 PROJECT 北京示范区置业（河北）项目（一期）基础设施项目——一期部分（一标段）

图名 DRAWING TITLE -0.100~6.750标高柱平面布置图

校审编号 JOB NO.	2021SJ/2526S	阶段 STAGE	施工图
比例 SCALE	1:100	专业 DISCIPLINE	结构
日期 DATE	2022.09	图号 DRAWING NO.	FG-SJ(X1-10

特发号